


2 M

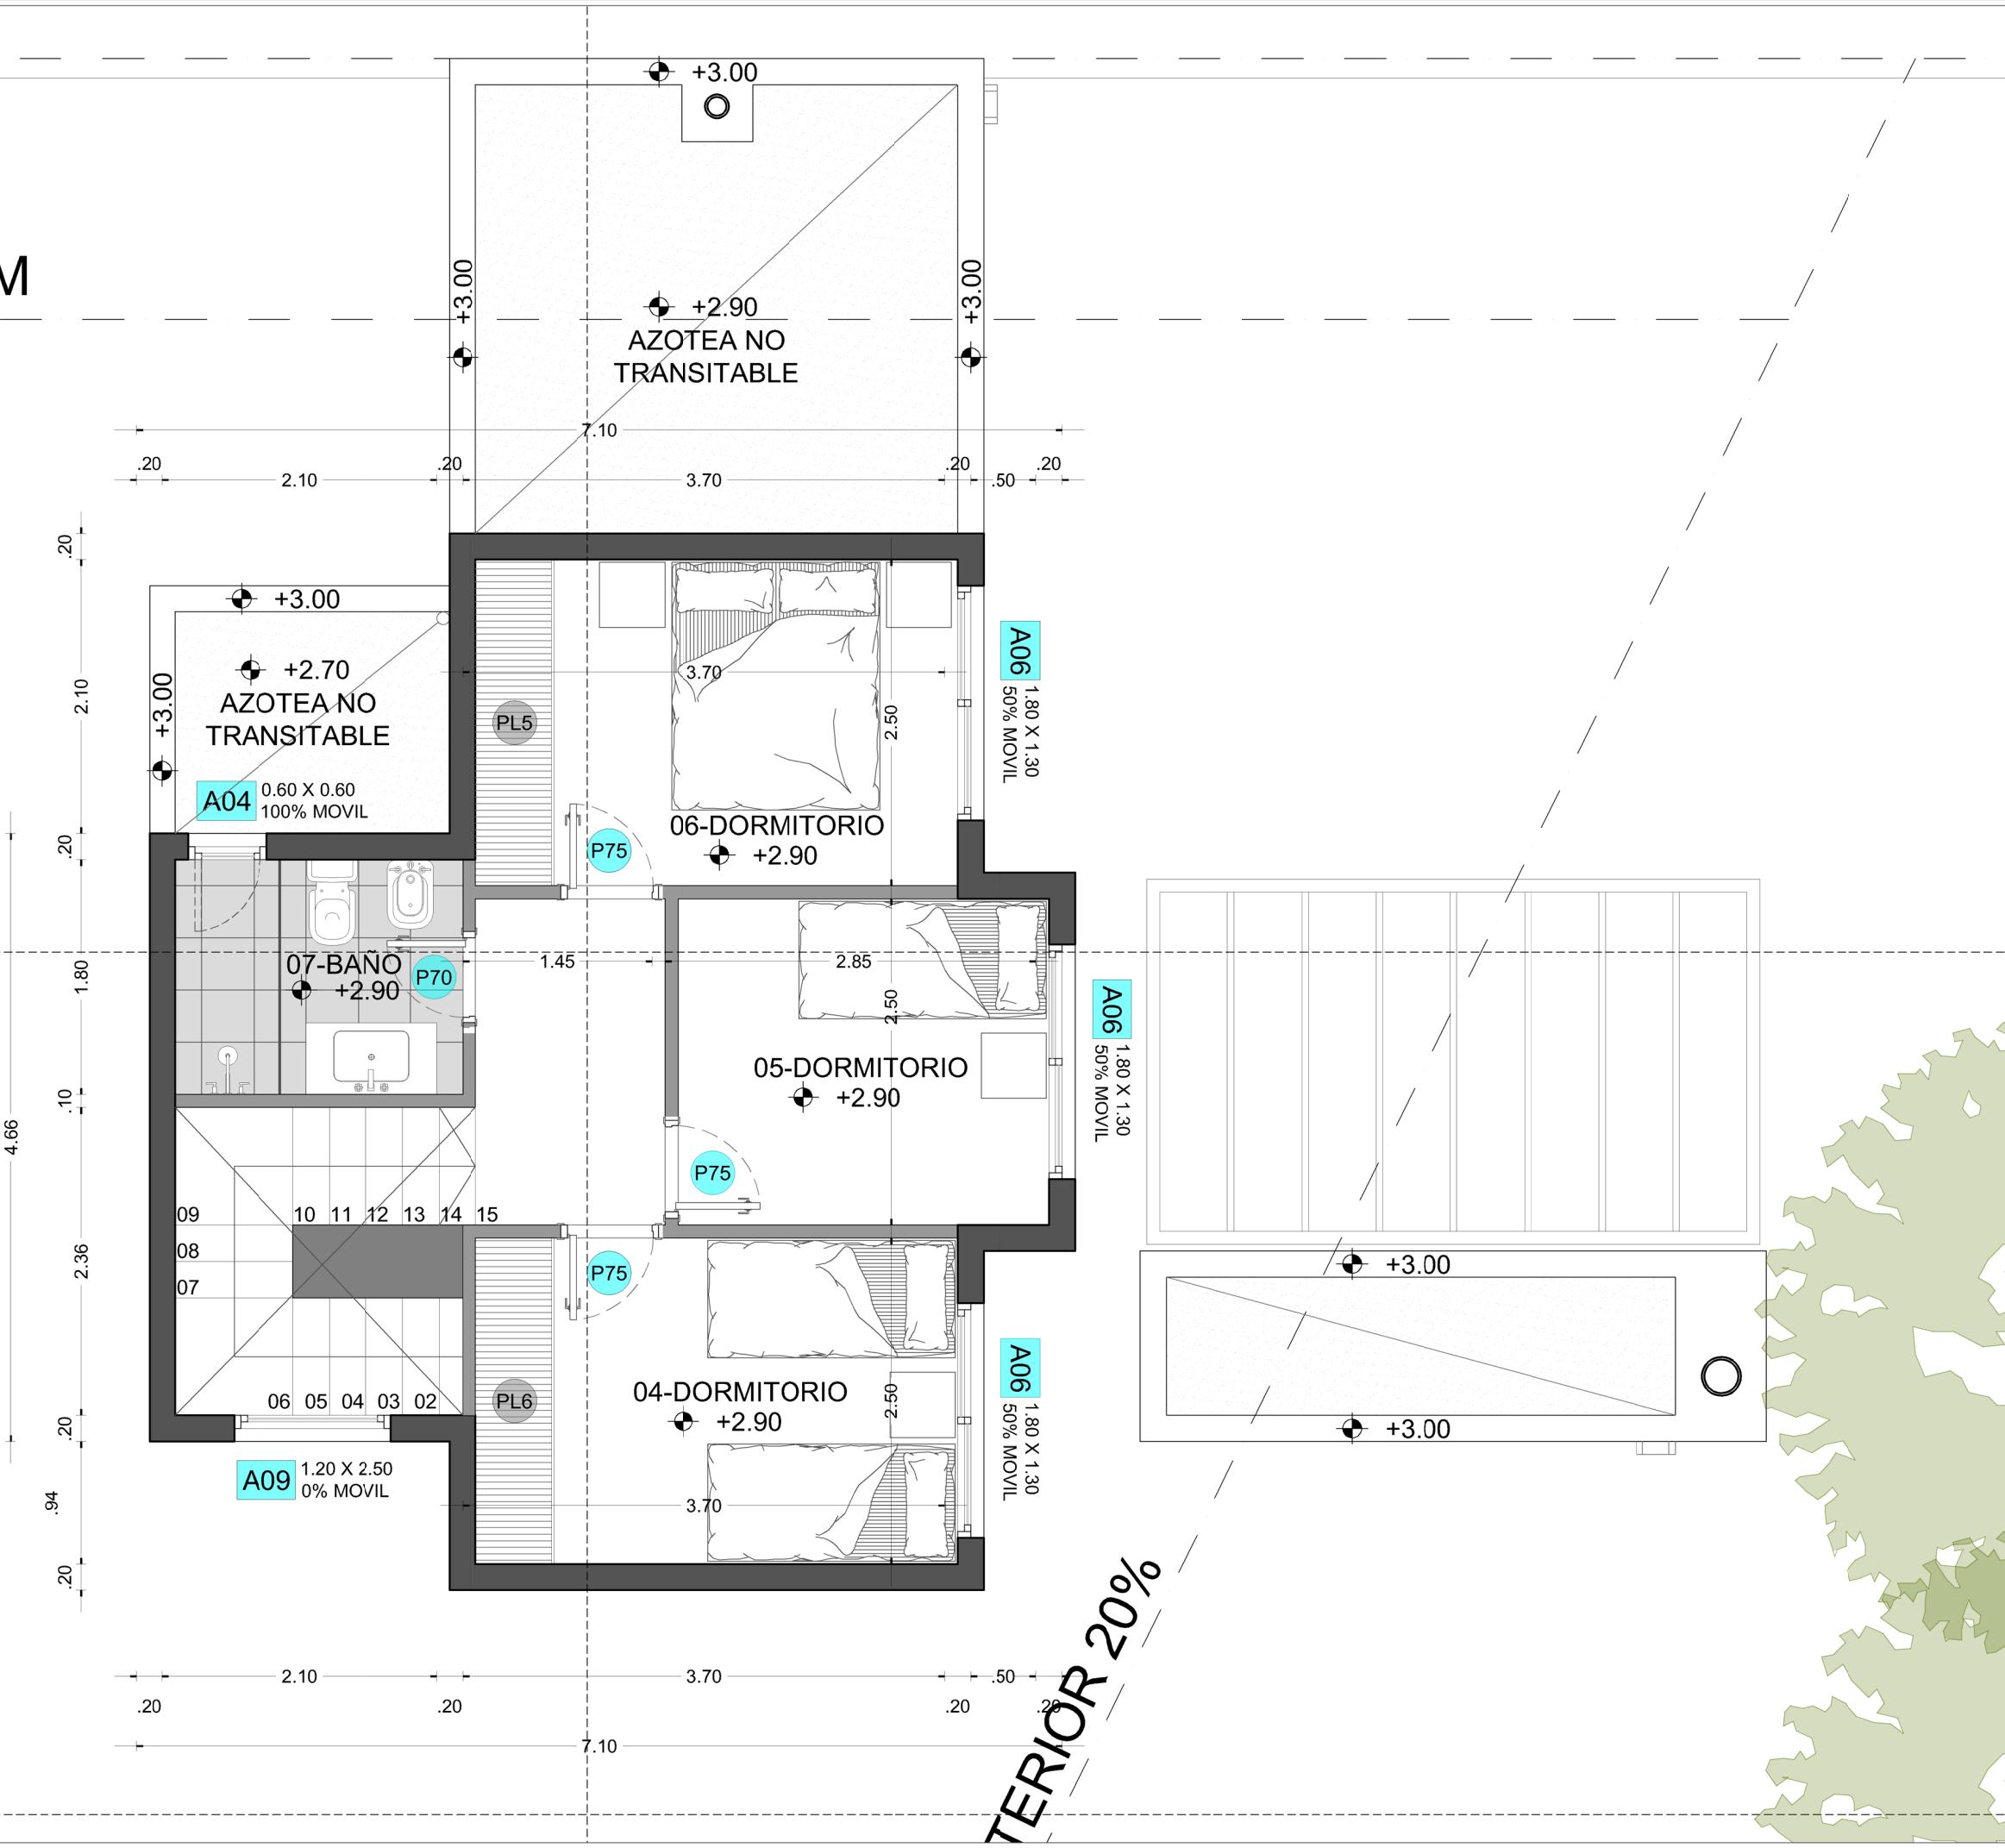

**INTERIOR 20%**

# ALBAÑILERIA

**JorgeSerra SebastiánDíaz**  
ARQUITECTOS

## **LOGIA EN DETALLE**

## **LOGIA 2 PLANTA ALTA**

REV 06 23-12-2020 1/50 AL12

