


ALBAÑILERIA

Jorge Serra Sebastián Díaz ARQUITECTOS 

REV 06

23-12-2020

AI 08

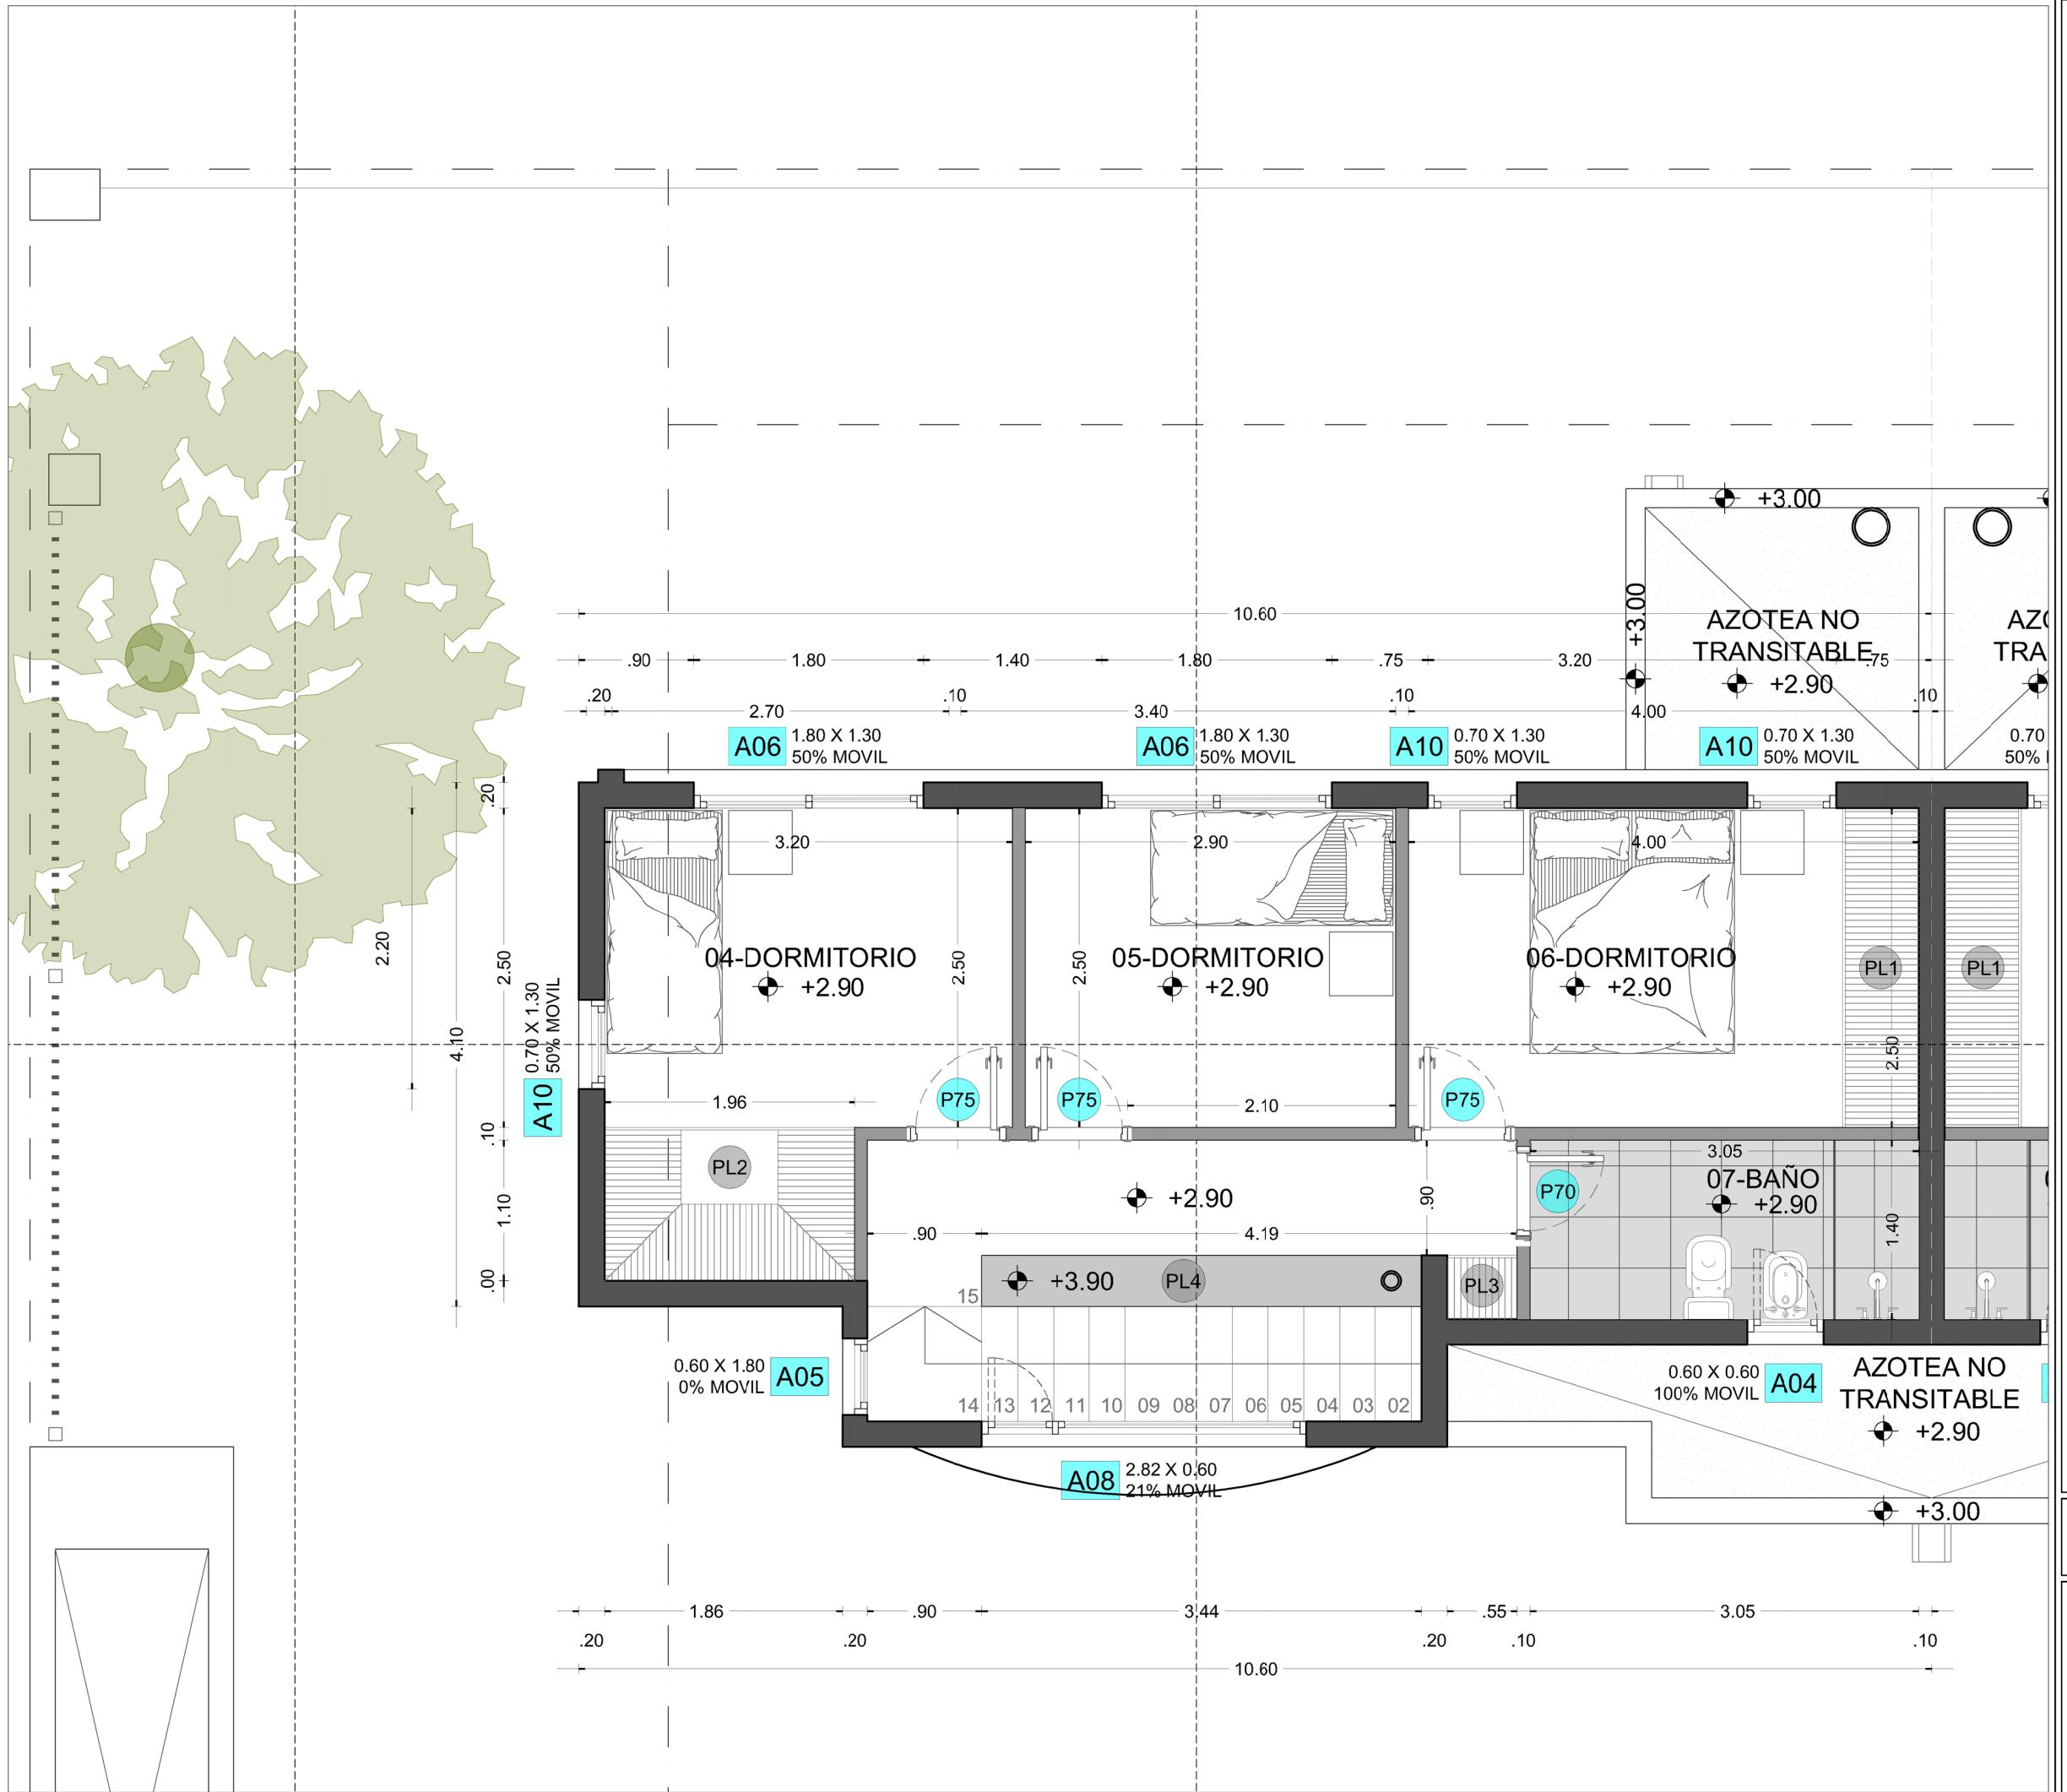


ALBAÑILERIA

Diseño de Construcción DiUringuer Gruo Jorge Serra Sebastián Díaz ARQUITECTOS

LAMINA TIPOLOGIA EN DETALLE TIPOLOGIA 1 PLANTA ALTA

REV 06 FECHA 23-12-2020 ESCALA 1/50 N° AL09

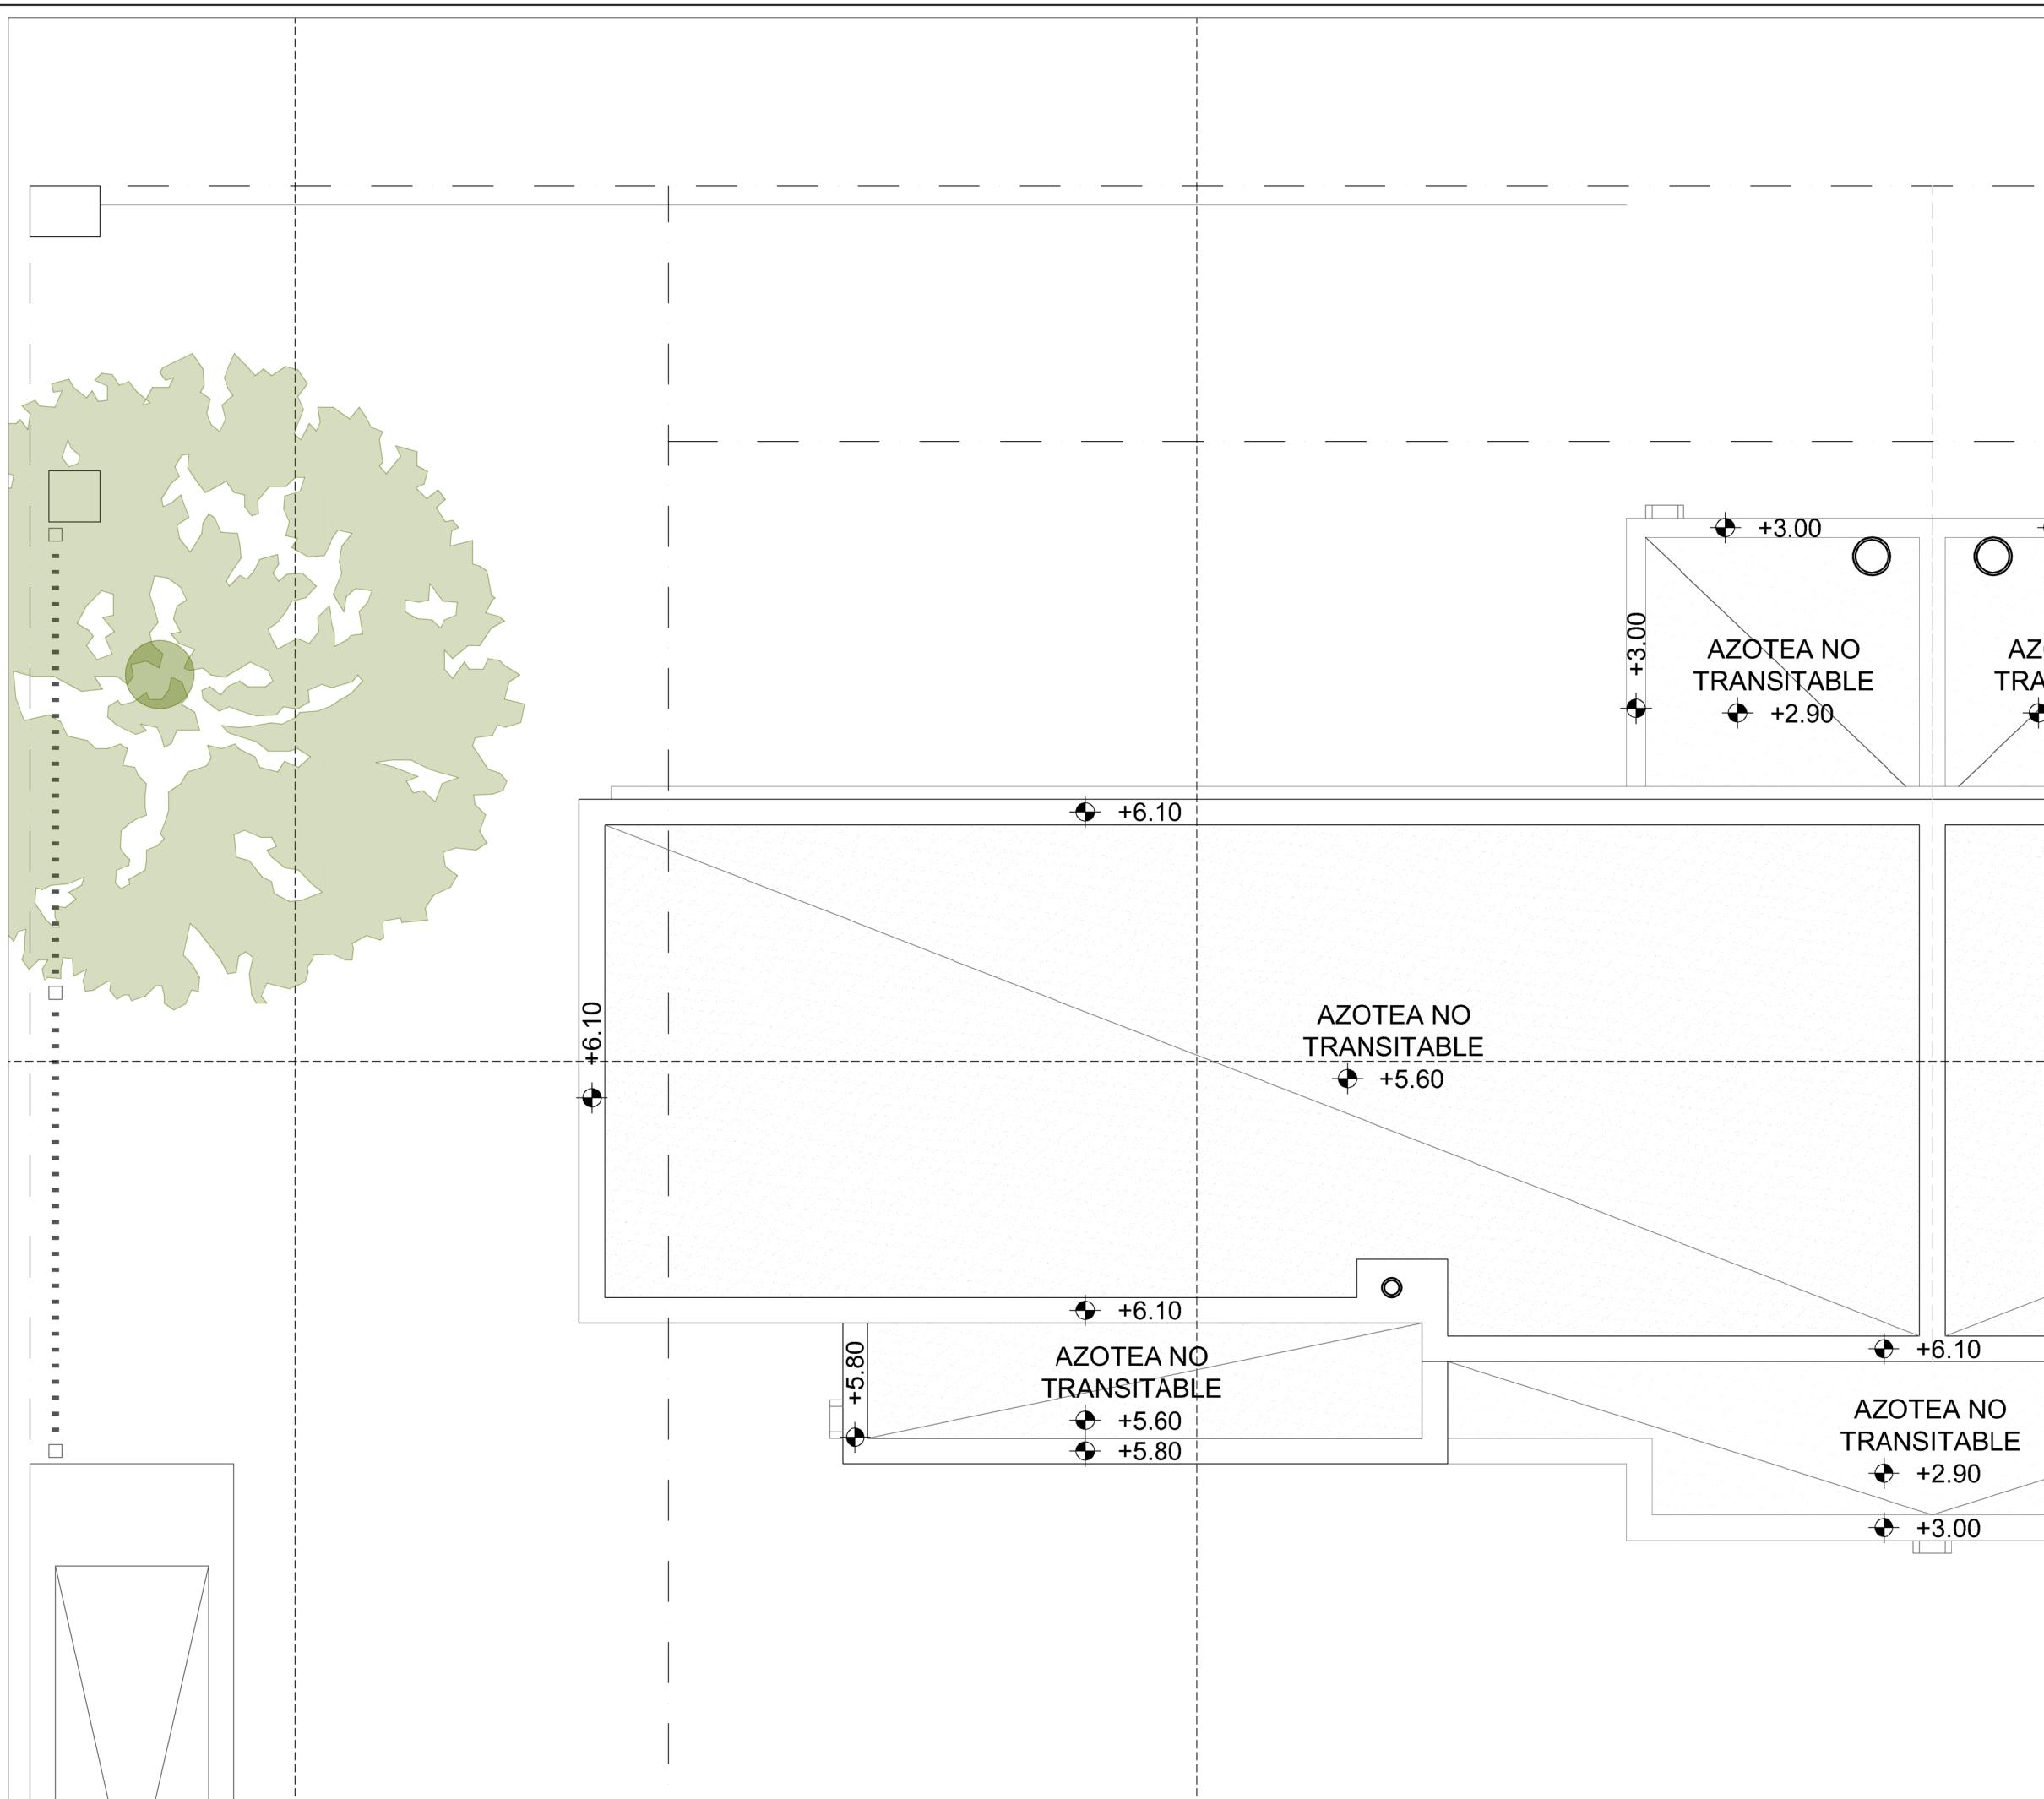

ALBAÑILERIA

Desarrollado por DiUringuer Gruo
Jorge Serra Sebastián Díaz
ARQUITECTOS

LAMINA
TIPOLOGIA EN DETALLE
TIPOLOGIA 1 PLANTA TECHOS

FECHA	ESCALA	Nº
23-12-2020	1/50	AL10

REV 06